
План

М 1 : 250 · осі тому КБ: x від осі 1 на схід, y від осі A на північ

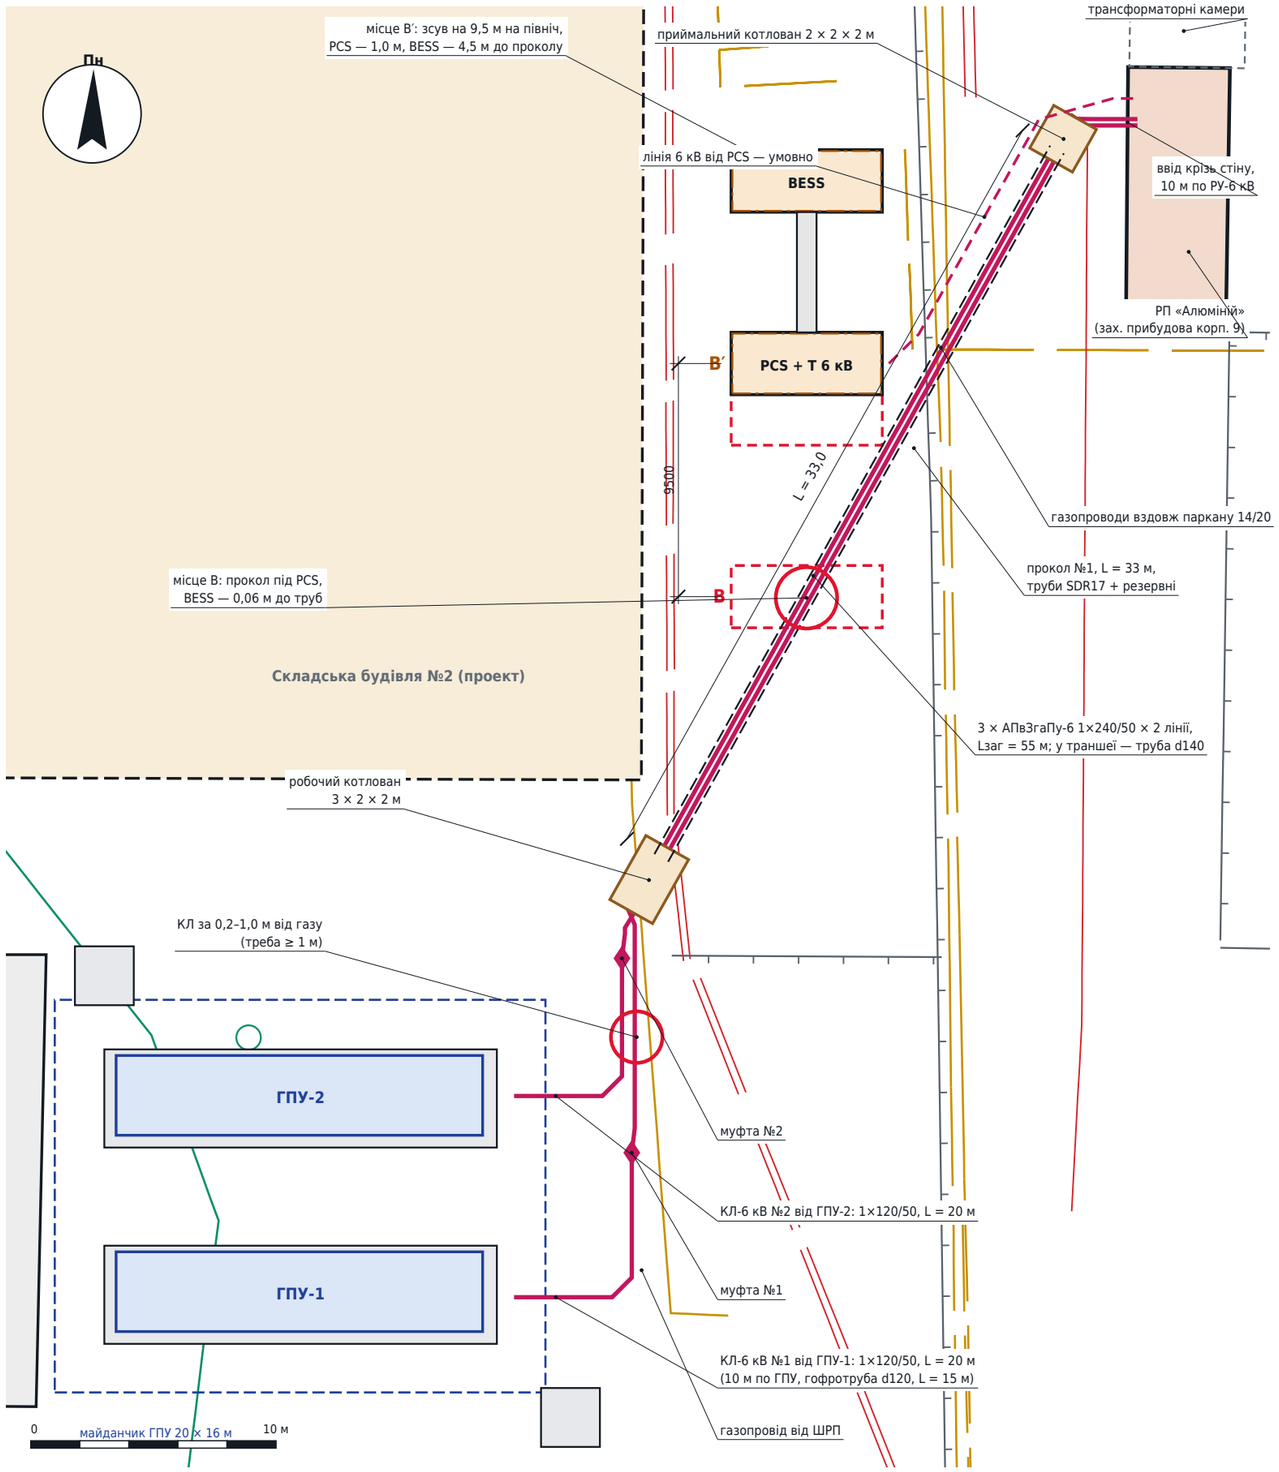

Перевірка відстаней за ПУЕ, гл. 2.3

у світлі; глибини існуючих мереж умовні (газ 1,2 м, кабелі 0,8 м) — потрібні шурфи

ЕСКІЗ · НЕ ДЛЯ БУДІВНИЦТВА

Що перевірено	Норма, пункт ПУЕ	У моделі	Висновок
Глибина траншеї до верху труби	≥ 0,7 м · 2.3.84	0,83 м	так
Газопровід від ШРП, паралельно	≥ 1 м · 2.3.88	0,21–0,97 м	НІ
Той самий газопровід, перетин біля котлована	≥ 0,25 м у трубі · 2.3.95	≈ 0,00 м	НІ
Газопроводи біля паркану 14/20, прокол	≥ 0,25 м у трубі · 2.3.95	0,27–0,28 м	межа
Кабель 6 кВ, перетин проколом	≥ 0,15 м з розділенням · 2.3.94	0,71 м	так
Кабелі 6 кВ поруч, паралельно	≥ 0,1 м · 2.3.86	не зближ.	так
Складська будівля №2 (проект)	≥ 0,6 м · 2.3.85	2,10 м	так
РП «Алюміній», крім вводу	≥ 0,6 м · 2.3.85	1,96 м	так
Плити Фпм-1 під ГПУ	≥ 0,6 м · 2.3.85	0,63 м	так
Фундаменти, місце B: PCS / BESS	≥ 0,6 м · 2.3.85	під PCS / 0,06 м	НІ
Фундаменти, місце B′: PCS / BESS	≥ 0,6 м · 2.3.85	1,00 / 4,54 м	так
Муфта №2 до КЛ №1	≥ 0,25 м · 2.3.100	0,60 м	так

Умовні позначення


- нові КЛ-6 кВ за кресленням траси
- межі пучка труб проколу
- водопровід
- інші кабелі
- BESS і PCS на місці B′ (запропоновано)
- порушення норми
- лінія 6 кВ від PCS — умовно
- газопровід (генплан 2023)
- кабелі 6 кВ існуючі
- BESS на місці B (вибране раніше)
- з'єднувальна муфта
- котлован

Примітки

1. Трасу знято зі знімку креслення траси КЛ-6 кВ (телефон, 21.10.2026). Знімок прив'язано за майданчиком ГПУ 20 × 16 м: масштаб 18,93 пкс/м, поворот 1,49°. Точність ±1 м. Газопроводи біля паркану 14/20 і будівля №2 зі знімку лягають на генплан з розбіжністю до 0,7 м, довжина КЛ №2 (≈ 53 м разом з опусканням у котловани і 10 м по РУ) відповідає підпису Lзаг = 55 м.
2. РП «Алюміній» — західна двоповерхова прибудова алюмінієвого корпусу 9: приймальний котлован стоїть під її західною стіною. Креслень РП у матеріалах немає.
3. ГПУ стоять як у томі КБ. На кресленні траси ГПУ-1 показано дзеркально до ГПУ-2 (обладнання на даху — з південного боку). У томі КБ плити однакові, отвір 600 × 400 під кабелі — біля південного краю кожної.
4. Місце B несумісне з трасою: прокол проходить під блоком PCS. Запропоновано місце B′ — той самий комплект на 9,5 м північніше; його фундаменти — на аркушах 3–6.
5. КЛ від муфт до робочого котлована йде впритул до газопроводу від ШРП, котлован — на ньому. Звірити з оригіналом креслення; за потреби відсунути КЛ на захід або погодити з газовою службою.
6. Перед проколом і копанням котлованів шурфами уточнити положення і глибину газопроводів і кабелів (усі глибини існуючих мереж на генплані умовні).

Об'єкт: **ТзДВ «Гал-Кат», площадка № 20. ГПУ, УЗЕ 1,725 МВт / 5 МВт·год**	Стадія: **Ескіз**
Аркуш: **Траса КЛ-6 кВ від ГПУ до РП «Алюміній» План з BESS і мережами, перевірка за ПУЕ**	Масштаб: **1 : 250**
Джерела: креслення траси КЛ-6 кВ (знімок 21.10.2026), том 4 КБ 15/2026-02-КБ, генплан 2023, Golen Annex 1, 3D-модель площадки	Дата: **21.10.2026**
	Аркуш: **1 / 6**


Поздовжній профіль КЛ-6 кВ №2 М гор. 1 : 250, верт. 1 : 50 · від виходу з ГПУ-2 до стіни РП

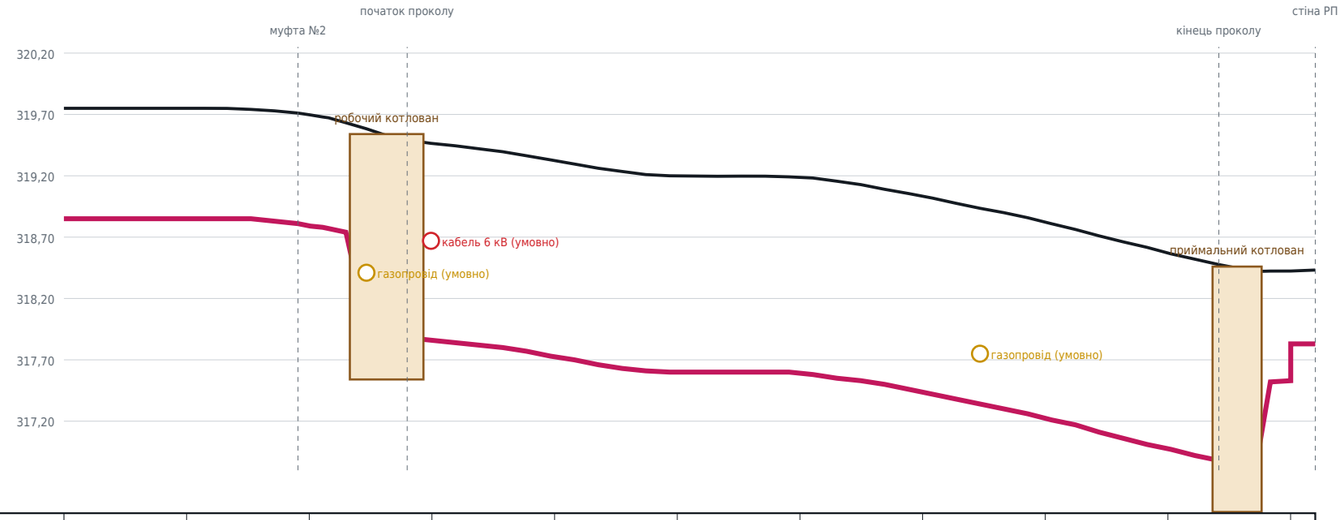


Земля, м	319,75	319,75	319,70	319,46	319,32	319,20	319,19	319,04	318,82	318,57	318,42
Вісь труби, м	318,85	318,85	318,79	317,86	317,72	317,60	317,59	317,44	317,22	316,98	317,53
Глибина осі, м	0,90	0,90	0,91	1,60	1,60	1,60	1,60	1,60	1,60	1,59	0,89
Пікет, м	0,0	5,0	10,0	15,0	20,0	25,0	30,0	35,0	40,0	45,0	50,0

Переріз траншеї М 1 : 20

ЕСКІЗ · НЕ ДЛЯ БУДІВНИЦТВА

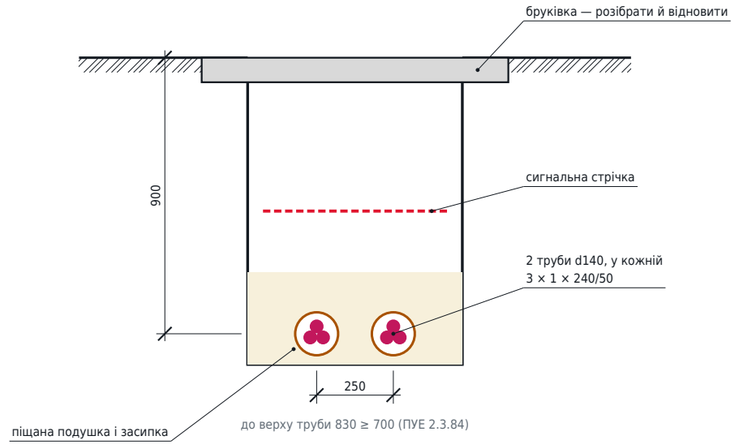

Переріз проколу М 1 : 20

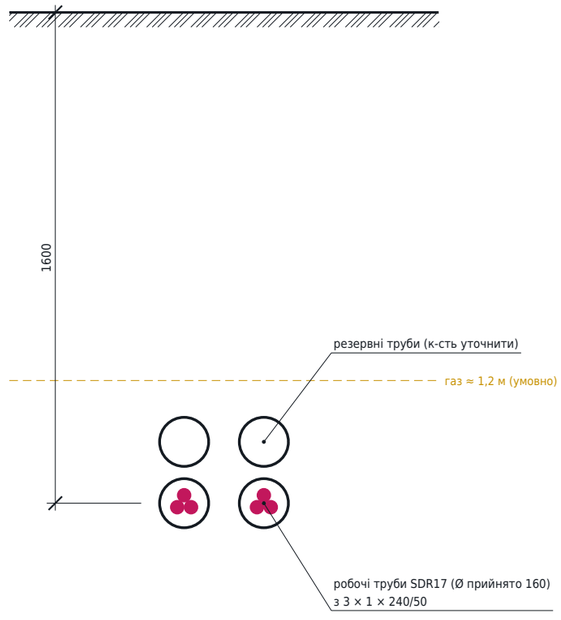

Фундамент BESS і PCS: два варіанти (на 1 фундамент; усього 2 — BESS і PCS)


Позиція	Варіант 1 як у Golen	Варіант 2 глибина 1,5 м	Різниця
Низ обв’язувальної балки	−1,850	−1,500	+0,350
Висота колон і кладки	1,80 м	1,45 м	−0,35 м
Бетон C25: балка 350 × 350	1,96 м³	1,96 м³	—
Бетон C25: колони 8 шт.	1,76 м³	1,42 м³	−0,34 м³
Бетон C25 разом	**3,72 м³**	**3,38 м³**	**−0,34 м³**
Цегляна кладка, M20	8,31 м³	6,69 м³	−1,62 м³
Площа кладки	23,7 м²	19,1 м²	−4,6 м²
Підготовка C8/10, 100 мм	0,88 м³	0,88 м³	—
Сталь (арк. 4 / 6)	**≈ 300 кг**	**≈ 282 кг**	**−18 кг**
Тиск під балкою (BESS 43 т)	≈ 120 кПа	≈ 110 кПа	—
Креслення	аркуші 3, 4	аркуші 5, 6	

Примітки

1. Обидва варіанти — та сама конструкція Golen: обв’язувальна балка 350 × 350 внизу, 8 колон 350 × 350 і цегляна кладка між ними; у варіанті 2 підошву піднято на 350 мм.
2. Позначки — від середньої позначки землі під блоком: місце В′ — 318,85 (BESS) і 319,12 (PCS). Різницю рельєфу між блоками (≈ 0,27 м) вирівняти плануванням.
3. Вибір варіанта — за розрахунком основи і нормативною глибиною промерзання для ґрунтів площадки (ДБН В.2.1-10, вишукування). Фундамент PCS прийнято того самого типу: Golen його не дав.
4. Від проколу до фундаментів на місці В′ — 1,0 м (PCS) і 4,5 м (BESS) у плані; прокол іде глибше за підошву обох варіантів, тож при проколі контролювати положення головки.


Об’єкт **ТзДВ «Гал-Кат», площадка № 20. ГПУ, УЗЕ 1,725 МВт / 5 МВт·год**	Стадія: **Ескіз**
Аркуш **Профіль траси КЛ-6 кВ №2, перерізи** **Порівняння варіантів фундаменту BESS / PCS**	Масштаб: **1 : 250 / 1 : 50; 1 : 20**
	Дата: **21.10.2026**
Джерела: креслення траси КЛ-6 кВ (знімок 21.10.2026), рельєф і мережі — 3D-модель площадки, фундаменти — Golen Annex 1	Аркуш: **2 / 6**

План фундаменту М 1 : 40 (контейнер умовно знято)

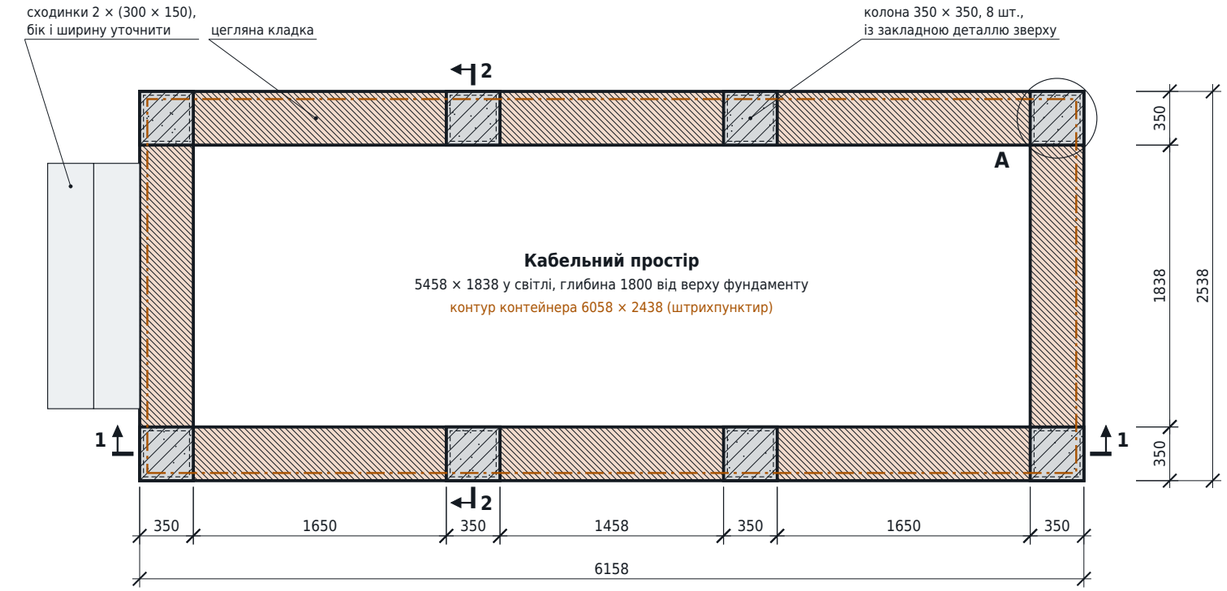

Вузол А М 1 : 10


ЕСКІЗ · НЕ ДЛЯ БУДІВНИЦТВА

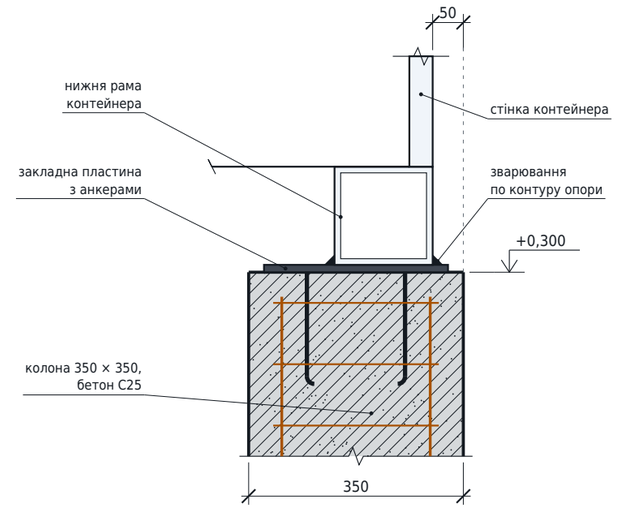


Умовні позначення

- залізобетон у розрізі
- цегляна кладка у розрізі
- ущільнений ґрунт основи
- природний ґрунт

1–1 М 1 : 40 (по осі поздовжньої стіни)

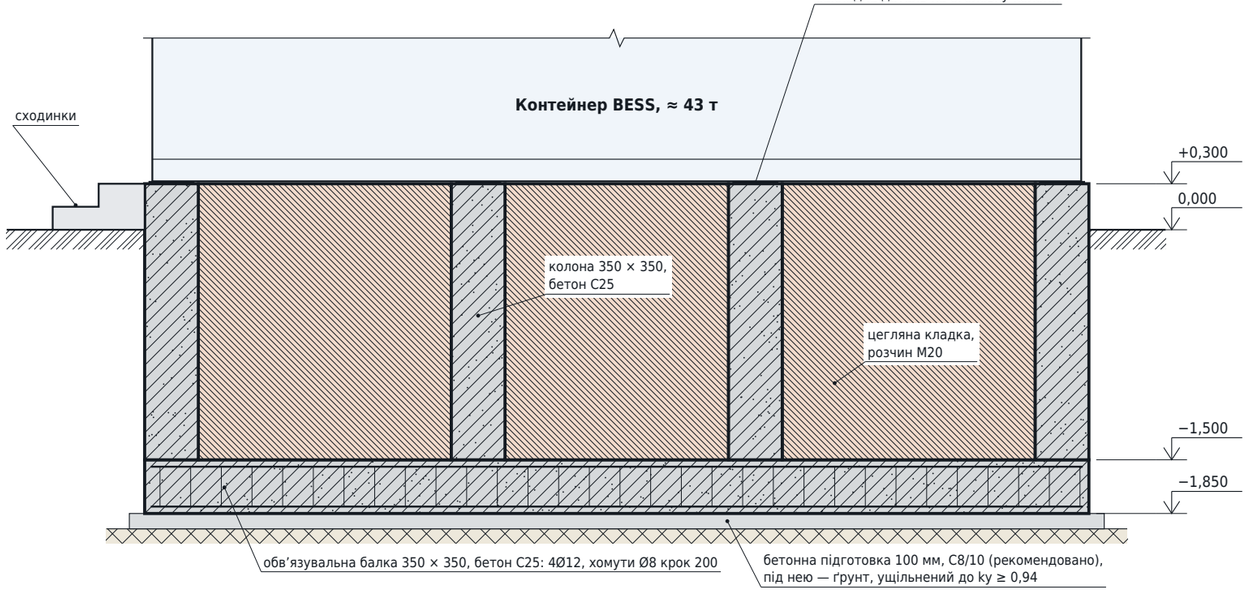

2–2 М 1 : 40

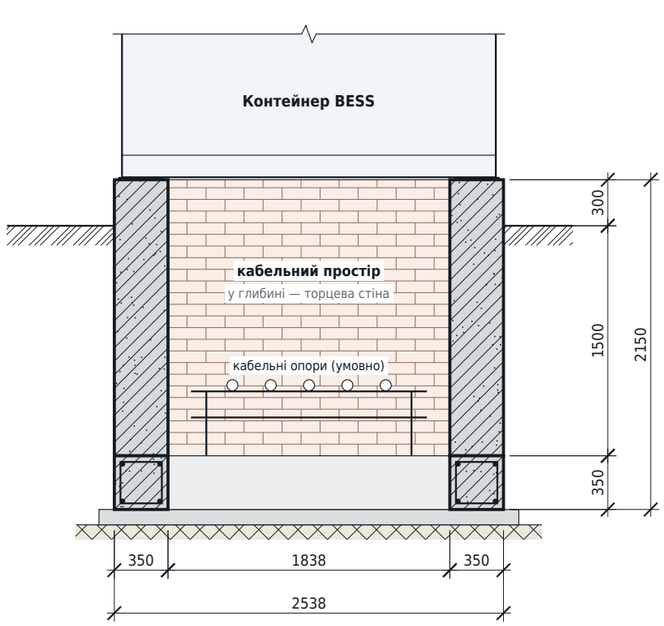

Горизонтальні розміри — за планом (розріз у проєкційному зв’язку з планом).

Обсяги (орієнтовно)

Бетон С25, балка 350 × 350	1,96 м³
Бетон С25, колони 8 шт.	1,76 м³
Бетон разом	3,72 м³
Кладка, площа стін (h = 1,80 м)	23,7 м²
Підготовка С8/10, 100 мм	0,88 м³
Сталь, усього (аркуш 4)	≈ 300 кг


Примітки

1. Варіант 1 — як у Golen: низ балки −1,850, колони 1800 мм. Ескіз — за довідковим кресленням Golen (Annex 1 – Response 1, Reference Foundation Drawing of 5MWh BESS Container). Фундамент блока PCS — того самого типу: Golen його не дав. Розміри в мм, позначки в м від верху землі біля блока.
2. Бетон С25 за позначенням виробника (орієнтовно С20/25). Балка 350 × 350: 4Ø12 поздовжні, хомути Ø8 з кроком 200. Армування колон, кутів і закладні деталі виробник не задав — пропозицію наведено на аркуші 4.
3. Основа — ущільнений ґрунт, коефіцієнт ущільнення не менше 0,94. Під балкою рекомендую бетонну підготовку 100 мм С8/10: без неї захисний шар 40 мм не забезпечити (аркуш 4).
4. Між колонами — цегляна кладка на розчині М20 (позначення виробника). Товщину кладки на кресленні Golen не вказано, показано умовно 350 мм.
5. На оголовках колон — закладні деталі, раму контейнера приварити до них (вузол А). Розміри пластин і анкерів уточнити у виробника.
6. До заведення кабелів установити кабельні опори внизу фундаменту. Отвори для вводу кабелів і відведення води з кабельного простору на кресленні Golen не показані — передбачити проєктом.
7. Сходинки показано з боку торцевих дверей контейнера. Бік розміщення і ширину уточнити.
8. Орієнтовний тиск під підошвою балки ≈ 120 кПа (контейнер BESS 43 т і власна вага фундаменту ≈ 24 т на площу ≈ 5,6 м²). Перевірити за ґрунтовими умовами; глибину закладання звірити з нормативною глибиною промерзання (ДБН В.2.1-10) і вишукуваннями.
9. Креслення є ескізом і не замінює робочу документацію. Перед бетонуванням потрібні підтвердження Golen і розрахунок проєктувальника.

Об’єкт	**ТзДВ «Гал-Кат», площадка № 20. ГПУ, УЗЕ 1,725 МВт / 5 МВт·год**
Аркуш	**Фундамент BESS і PCS · варіант 1 План, розрізи 1–1 і 2–2, вузол А**
Джерело геометрії: Golen Power Technology, Annex 1 – Response 1 (довідкові креслення)	
Стадія	**Ескіз**
Масштаб	**1 : 40; 1 : 10**
Дата	**21.10.2026**
Аркуш	**3 / 6**


Армування обв’язувальної балки

М 1 : 40 · план на рівні балки

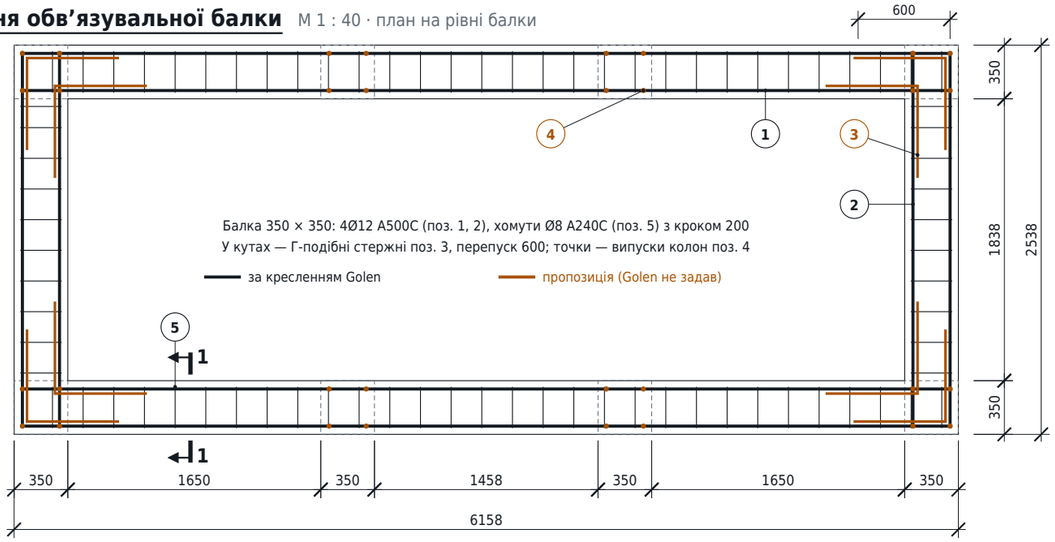


Каркас колони

М 1 : 20 · розріз уздовж балки

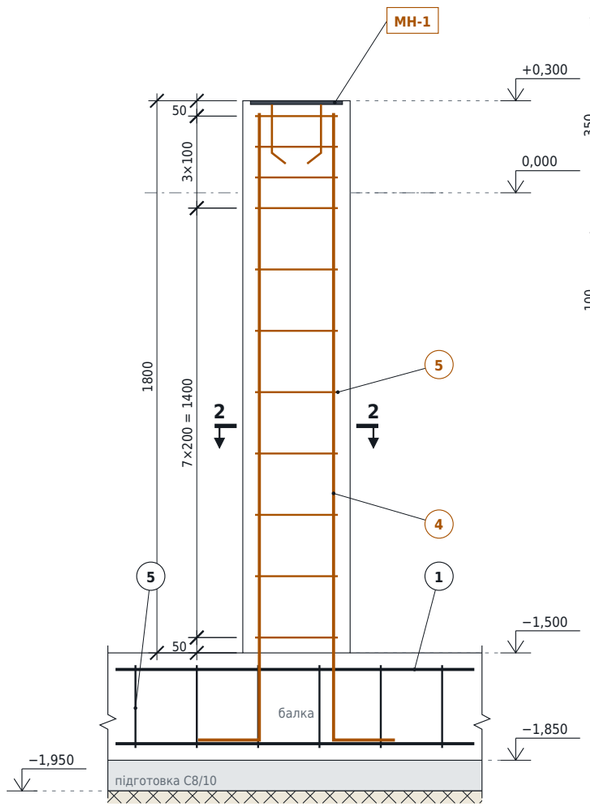


1–1

М 1 : 10

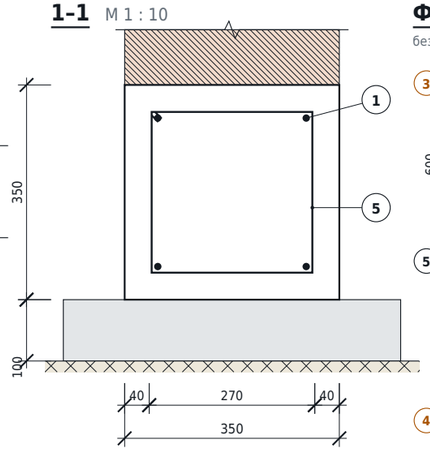

2–2

М 1 : 10

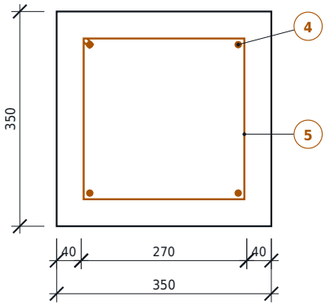

Форми стержнів

без масштабу, розміри в мм



Специфікація арматури

кількість і маса — на 1 виріб

ЕСКІЗ · НЕ ДЛЯ БУДІВНИЦТВА

Поз.	Позначення	Найменування	К-сть	Маса од., кг	Примітка
Фундамент контейнера, на 1 шт. (усього 2: BESS і PCS — умовно)					
1	ДСТУ 3760:2019	Ø12 A500C, L = 6080	8	5,40	балка, поздовжні
2	ДСТУ 3760:2019	Ø12 A500C, L = 2460	8	2,18	балка, торці
3	ДСТУ 3760:2019	Ø12 A500C, L = 1200 (Г 600 × 600)	16	1,07	кути балки
4	ДСТУ 3760:2019	Ø12 A500C, L = 2240 (Г 2040 + 200)	32	1,99	колони, 4 на колону
5	ДСТУ 3760:2019	Ø8 A240C, L = 1240 (хомут 270 × 270)	172	0,49	84 балка + 88 колони
МН-1	—	лист 300×300×12 С245, анкери 4Ø12 A500C, L = 230	8	9,29	уточнити в Golen
Кабельний канал, монолітний, L = 4900, 1 шт.					
6	ДСТУ 3760:2019	Ø8 A500C, L = 1640 (П 470 + 700 + 470)	25	0,65	крок 200
7	ДСТУ 3760:2019	Ø8 A500C, L = 4840	8	1,91	4 у дні, по 2 у стінах
Плита перекриття П-1, 800 × 478 × 80, на 1 шт. (усього 10)					
8	ДСТУ 3760:2019	Ø8 A500C, L = 750	4	0,30	поперечні, знизу
9	ДСТУ 3760:2019	Ø8 A500C, L = 430	5	0,17	поздовжні
Перемичка ПР-1 над вводом каналу, 900 × 350 × 120, на 1 шт. (усього 2)					
10	ДСТУ 3760:2019	Ø10 A500C, L = 860	3	0,53	нижні
11	ДСТУ 3760:2019	Ø6 A240C, L = 310	5	0,07	поперечні

Відомість витрати сталі й бетону


сталь у кг, бетон у м³

Елемент	Ø12 A500C	Ø10 A500C	Ø8 A500C	Ø8 A240C	Ø6 A240C	Закладні МН-1	Сталь разом	Бетон
Фундамент BESS	141,4	—	—	84,2	—	74,4	300,0	3,72 C25
Фундамент PCS (умовно)	141,4	—	—	84,2	—	74,4	300,0	3,72 C25
Бетонна підготовка, 2 шт.	—	—	—	—	—	—	—	1,76 C8/10
Кабельний канал	—	—	31,5	—	—	—	31,5	0,83 C25
Плити П-1, 10 шт.	—	—	20,3	—	—	—	20,3	0,31 C25
Перемички ПР-1, 2 шт.	—	3,2	—	—	0,7	—	3,9	0,08 C25
Разом	**282,7**	**3,2**	**51,8**	**168,5**	**0,7**	**148,7**	**655,7**	**10,42**

Бетон: C25 — 8,66 м³, підготовка C8/10 — 1,76 м³. Маса сталі — без відходів і в’язального дроту.


Кабельний канал: армування

М 1 : 10 · кабелі не показано

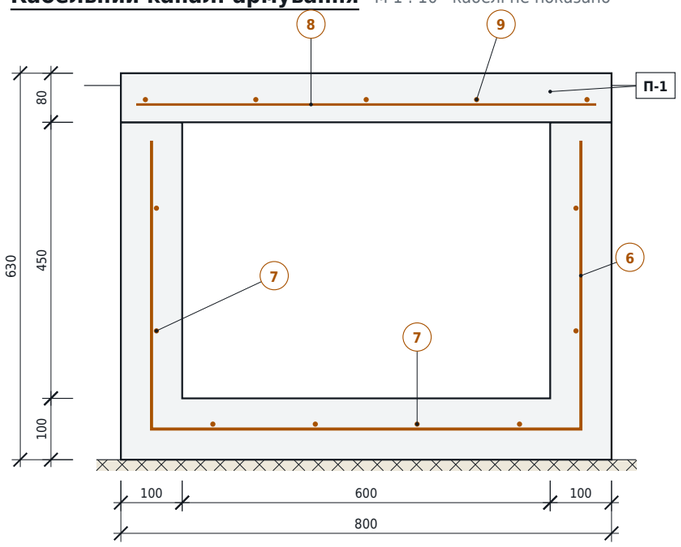


Плита П-1

М 1 : 20 · план

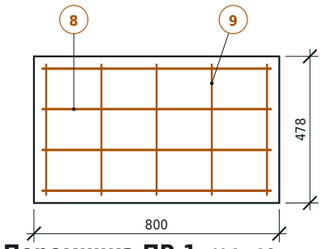

Перемичка ПР-1

М 1 : 10 · переріз

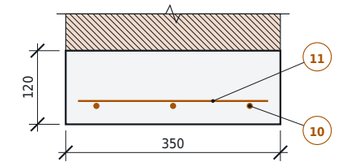


над отвором 600 × 450 у кладці

Примітки

1. Чорним — армування балки за кресленням Golen (4Ø12, хомути Ø8 з кроком 200). Помаранчевим — те, чого Golen не задав: кутові стержні, колони, закладні деталі, а також канал, плити й перемички (мій попередній розрахунок). Усе перевірити розрахунком проєктувальника.
2. Арматура за ДСТУ 3760:2019: A500C — поздовжня, A240C — хомути й Ø6. Бетон C25 (≈ C20/25), підготовка — C8/10.
3. Захисний шар до хомутів 40 мм — лише з бетонною підготовкою 100 мм під балкою. Якщо бетонувати просто по ґрунту, захисний шар знизу потрібен 70–75 мм, і переріз 350 × 350 стає затісним.
4. Стержні балки не стикувати по довжині; у кутах — Г-подібні стержні поз. 3 з перепуском 600 мм (50d). Хомути замкнені, з гаками 135°.
5. Випуски колон поз. 4 заводити в каркас балки до нижніх стержнів, лапкою 200 мм уздовж балки. Шов між балкою та колонами очистити й зробити шорстким.
6. Закладні МН-1 виставити на +0,300 за нівеліром до бетонування колон. Розміри пластин і анкерів погодити з Golen.
7. Плити П-1 лежать на стінках каналу насухо, їх можна виготовити заздалегідь. Канал проходить під зоною дверей трансформатора, тож плити мають витримувати прохід людей.
8. Маса в специфікації — без відходів на різання й в’язального дроту; на замовлення додати 3–5 %.


Об’єкт	**ТзДВ «Гал-Кат», площадка № 20. ГПУ, УЗЕ 1,725 МВт / 5 МВт·год**
Аркуш	**Армування фундаменту · варіант 1 Каркаси, специфікація, кабельний канал**
Джерело геометрії: Golen Power Technology, Annex 1 – Response 1 (довідкові креслення)	
Стадія	**Ескіз**
Масштаб	**1 : 40; 1 : 20; 1 : 10**
Дата	**21.10.2026**
Аркуш	**4 / 6**

План фундаменту М 1 : 40 (контейнер умовно знято)

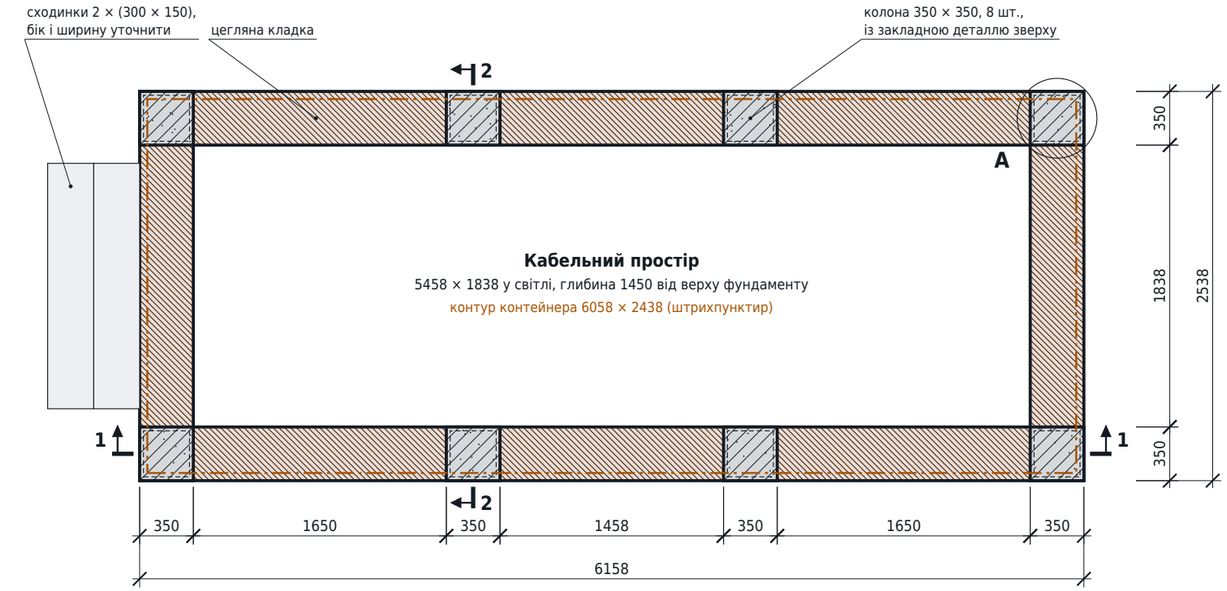

Вузол А М 1 : 10


ЕСКІЗ · НЕ ДЛЯ БУДІВНИЦТВА

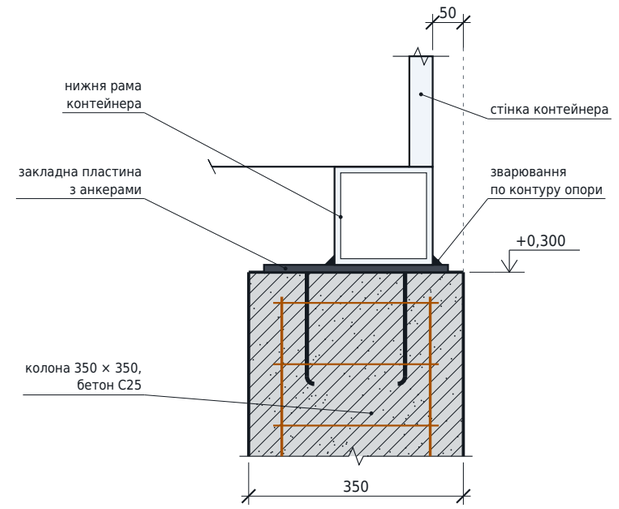


Умовні позначення

- залізобетон у розрізі
- цегляна кладка у розрізі
- ущільнений ґрунт основи
- природний ґрунт

1–1 М 1 : 40 (по осі поздовжньої стіни)

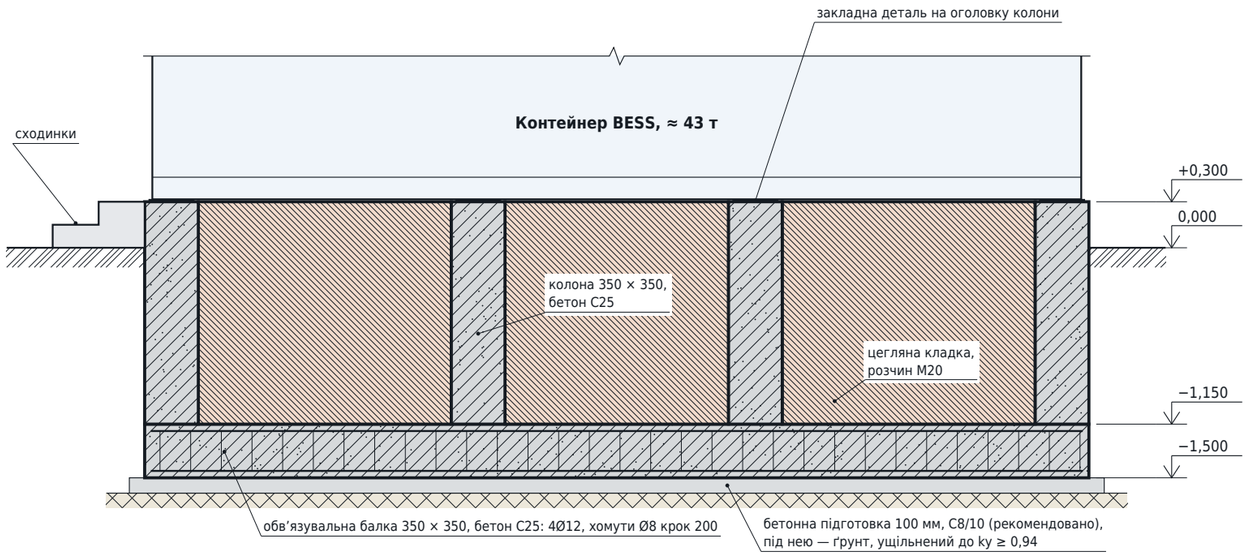

2–2 М 1 : 40

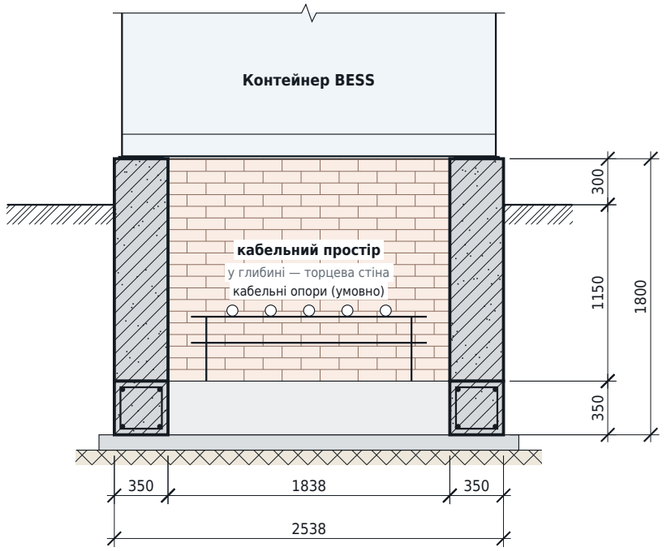

Горизонтальні розміри — за планом (розріз у проєкційному зв'язку з планом).

Обсяги (орієнтовно)

Бетон С25, балка 350 × 350	1,96 м³
Бетон С25, колони 8 шт.	1,42 м³
Бетон разом	3,38 м³
Кладка, площа стін (h = 1,45 м)	19,1 м²
Підготовка С8/10, 100 мм	0,88 м³
Сталь, усього (аркуш 6)	≈ 282 кг


Примітки

1. Варіант 2 — глибина 1,5 м: та сама конструкція, підошву піднято на 350 мм — низ балки −1,500, колони 1450 мм. Ескіз — за довідковим кресленням Golen (Annex 1 – Response 1, Reference Foundation Drawing of 5MWh BESS Container). Фундамент блока PCS — того самого типу: Golen його не дав. Розміри в мм, позначки в м від верху землі біля блока.
2. Бетон С25 за позначенням виробника (орієнтовно С20/25). Балка 350 × 350: 4Ø12 поздовжні, хомути Ø8 з кроком 200. Армування колон, кутів і закладні деталі виробник не задав — пропозицію наведено на аркуші 6.
3. Основа — ущільнений ґрунт, коефіцієнт ущільнення не менше 0,94. Під балкою рекомендую бетонну підготовку 100 мм С8/10: без неї захисний шар 40 мм не забезпечити (аркуш 6).
4. Між колонами — цегляна кладка на розчині М20 (позначення виробника). Товщину кладки на кресленні Golen не вказано, показано умовно 350 мм.
5. На оголовках колон — закладні деталі, раму контейнера приварити до них (вузол А). Розміри пластин і анкерів уточнити у виробника.
6. До заведення кабелів установити кабельні опори внизу фундаменту. Отвори для вводу кабелів і відведення води з кабельного простору на кресленні Golen не показані — передбачити проєктом.
7. Сходинки показано з боку торцевих дверей контейнера. Бік розміщення і ширину уточнити.
8. Орієнтовний тиск під підошвою балки ≈ 110 кПа (контейнер BESS 43 т і власна вага фундаменту ≈ 21 т на площу ≈ 5,6 м²). Перевірити за ґрунтовими умовами; глибину закладання звірити з нормативною глибиною промерзання (ДБН В.2.1-10) і вишукуваннями.
9. Креслення є ескізом і не замінює робочу документацію. Перед бетонуванням потрібні підтвердження Golen і розрахунок проєктувальника.

Об'єкт	**ТзДВ «Гал-Кат», площадка № 20. ГПУ, УЗЕ 1,725 МВт / 5 МВт·год**
Аркуш	**Фундамент BESS і PCS · варіант 2 План, розрізи 1–1 і 2–2, вузол А**
Джерело геометрії: Golen Power Technology, Annex 1 – Response 1 (довідкові креслення)	
Стадія	**Ескіз**
Масштаб	**1 : 40; 1 : 10**
Дата	**21.10.2026**
Аркуш	**5 / 6**


Армування обв’язувальної балки

М 1 : 40 · план на рівні балки

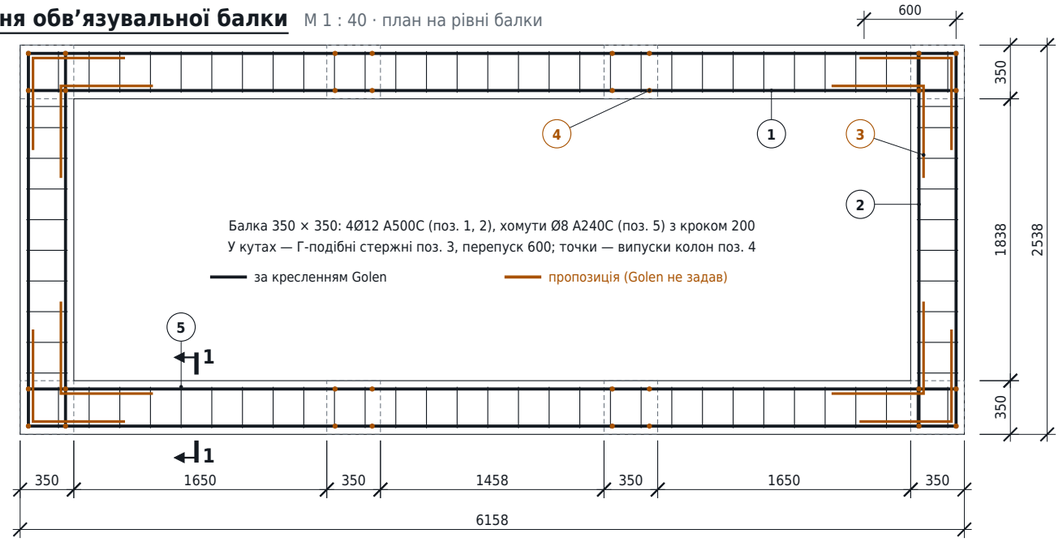


Каркас колони

М 1 : 20 · розріз уздовж балки

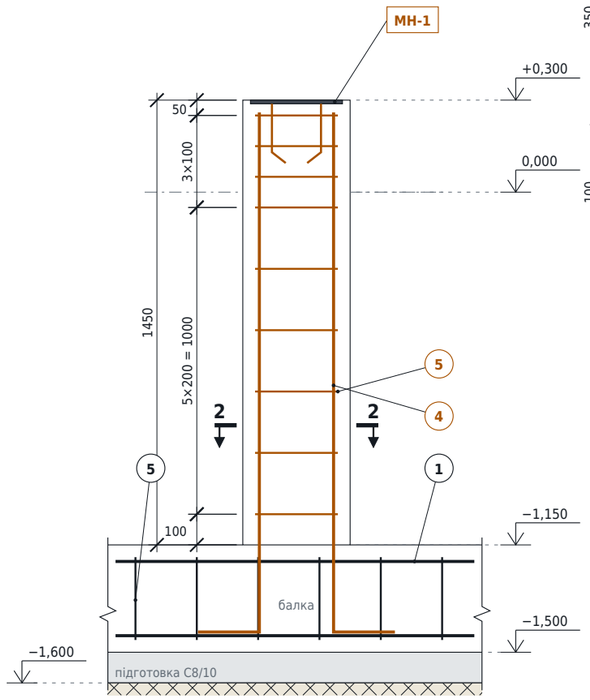


1–1

М 1 : 10

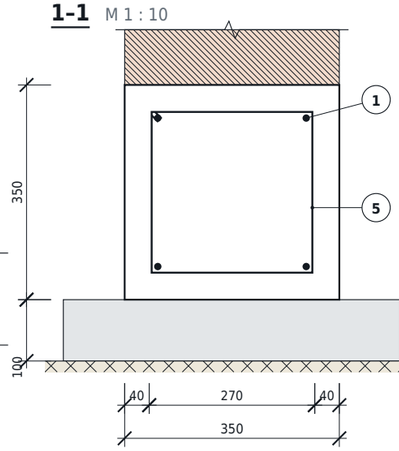

2–2


М 1 : 10

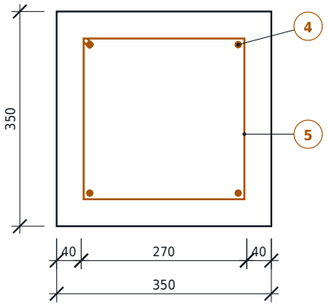


Форми стержнів

без масштабу, розміри в мм

3 Ø12 A500C, L = 1200

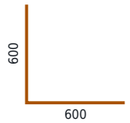

5 Ø8 A240C, L = 1240

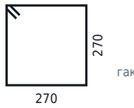

гаки 135°, 80

4 Ø12 A500C, L = 1890



у колону
лапка — у балку

6 Ø8 A500C, L = 1640



канал

МН-1 лист 300 × 300 × 12



4 анкери Ø12, L = 230

Специфікація арматури

кількість і маса — на 1 виріб

ЕСКІЗ · НЕ ДЛЯ БУДІВНИЦТВА

Поз.	Позначення	Найменування	К-сть	Маса од., кг	Примітка
Фундамент контейнера, на 1 шт. (усього 2: BESS і PCS — умовно)					
1	ДСТУ 3760:2019	Ø12 A500C, L = 6080	8	5,40	балка, поздовжні
2	ДСТУ 3760:2019	Ø12 A500C, L = 2460	8	2,18	балка, торці
3	ДСТУ 3760:2019	Ø12 A500C, L = 1200 (Г 600 × 600)	16	1,07	кути балки
4	ДСТУ 3760:2019	Ø12 A500C, L = 1890 (Г 1690 + 200)	32	1,68	колони, 4 на колону
5	ДСТУ 3760:2019	Ø8 A240C, L = 1240 (хомут 270 × 270)	156	0,49	84 балка + 72 колони
МН-1	—	лист 300×300×12 С245, анкери 4Ø12 A500C, L = 230	8	9,29	уточнити в Golen
Кабельний канал, монолітний, L = 4900, 1 шт.					
6	ДСТУ 3760:2019	Ø8 A500C, L = 1640 (П 470 + 700 + 470)	25	0,65	крок 200
7	ДСТУ 3760:2019	Ø8 A500C, L = 4840	8	1,91	4 у дні, по 2 у стінах
Плита перекриття П-1, 800 × 478 × 80, на 1 шт. (усього 10)					
8	ДСТУ 3760:2019	Ø8 A500C, L = 750	4	0,30	поперечні, знизу
9	ДСТУ 3760:2019	Ø8 A500C, L = 430	5	0,17	поздовжні
Перемичка ПР-1 над вводом каналу, 900 × 350 × 120, на 1 шт. (усього 2)					
10	ДСТУ 3760:2019	Ø10 A500C, L = 860	3	0,53	нижні
11	ДСТУ 3760:2019	Ø6 A240C, L = 310	5	0,07	поперечні

Відомість витрати сталі й бетону


сталь у кг, бетон у м³

Елемент	Ø12 A500C	Ø10 A500C	Ø8 A500C	Ø8 A240C	Ø6 A240C	Закладні МН-1	Сталь разом	Бетон
Фундамент BESS	131,4	—	—	76,4	—	74,4	282,2	3,38 C25
Фундамент PCS (умовно)	131,4	—	—	76,4	—	74,4	282,2	3,38 C25
Бетонна підготовка, 2 шт.	—	—	—	—	—	—	—	1,76 C8/10
Кабельний канал	—	—	31,5	—	—	—	31,5	0,83 C25
Плити П-1, 10 шт.	—	—	20,3	—	—	—	20,3	0,31 C25
Перемички ПР-1, 2 шт.	—	3,2	—	—	0,7	—	3,9	0,08 C25
Разом	**262,8**	**3,2**	**51,8**	**152,8**	**0,7**	**148,7**	**620,1**	**9,73**

Бетон: C25 — 7,97 м³, підготовка C8/10 — 1,76 м³. Маса сталі — без відходів і в’язального дроту.


Кабельний канал: армування

М 1 : 10 · кабелі не показано

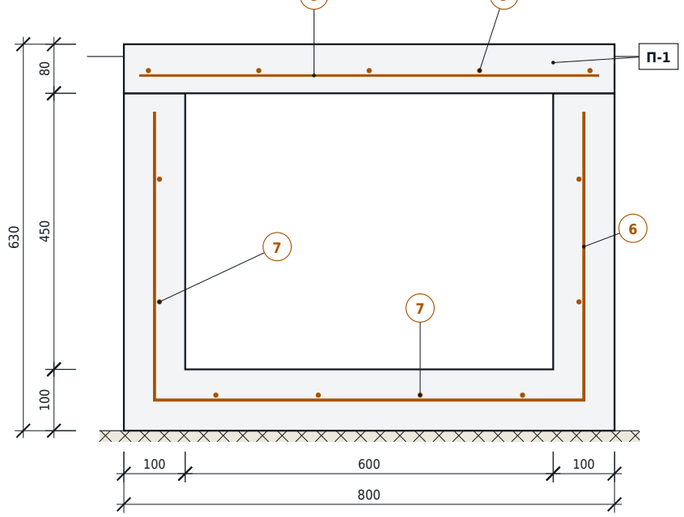


Плита П-1

М 1 : 20 · план

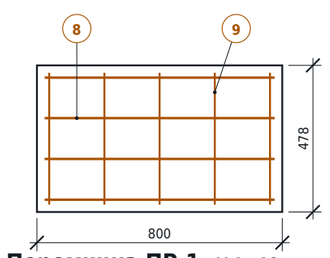

Перемичка ПР-1

М 1 : 10 · переріз

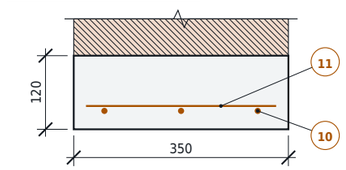

над отвором 600 × 450 у кладці

Примітки

1. Чорним — армування балки за кресленням Golen (4Ø12, хомути Ø8 з кроком 200). Помаранчевим — те, чого Golen не задав: кутові стержні, колони, закладні деталі, а також канал, плити й перемички (мій попередній розрахунок). Усе перевірити розрахунком проєктувальника.
2. Арматура за ДСТУ 3760:2019: A500C — поздовжня, A240C — хомути й Ø6. Бетон C25 (≈ C20/25), підготовка — C8/10.
3. Захисний шар до хомутів 40 мм — лише з бетонною підготовкою 100 мм під балкою. Якщо бетонувати просто по ґрунту, захисний шар знизу потрібен 70–75 мм, і переріз 350 × 350 стає затісним.
4. Стержні балки не стикувати по довжині; у кутах — Г-подібні стержні поз. 3 з перепуском 600 мм (50d). Хомути замкнені, з гаками 135°.
5. Випуски колон поз. 4 заводити в каркас балки до нижніх стержнів, лапкою 200 мм уздовж балки. Шов між балкою та колонами очистити й зробити шорстким.
6. Закладні МН-1 виставити на +0,300 за нівеліром до бетонування колон. Розміри пластин і анкерів погодити з Golen.
7. Плити П-1 лежать на стінках каналу насухо, їх можна виготовити заздалегідь. Канал проходить під зоною дверей трансформатора, тож плити мають витримувати прохід людей.
8. Маса в специфікації — без відходів на різання й в’язального дроту; на замовлення додати 3–5 %.

Об’єкт	**ТзДВ «Гал-Кат», площадка № 20. ГПУ, УЗЕ 1,725 МВт / 5 МВт·год**
Аркуш	**Армування фундаменту · варіант 2 Каркаси, специфікація, кабельний канал**
Джерело геометрії: Golen Power Technology, Annex 1 – Response 1 (довідкові креслення)	
Стадія	**Ескіз**
Масштаб	**1 : 40; 1 : 20; 1 : 10**
Дата	**21.10.2026**
Аркуш	**6 / 6**